S-4850
PURDUE-HILLEL MINOR SUBDIVISION, A REPLAT OF LOTS 2 & 3, STOCKTON'S PLAT OF WEST LAFAYETTE
(minor-sketch)

STAFF REPORT
June 13, 2019

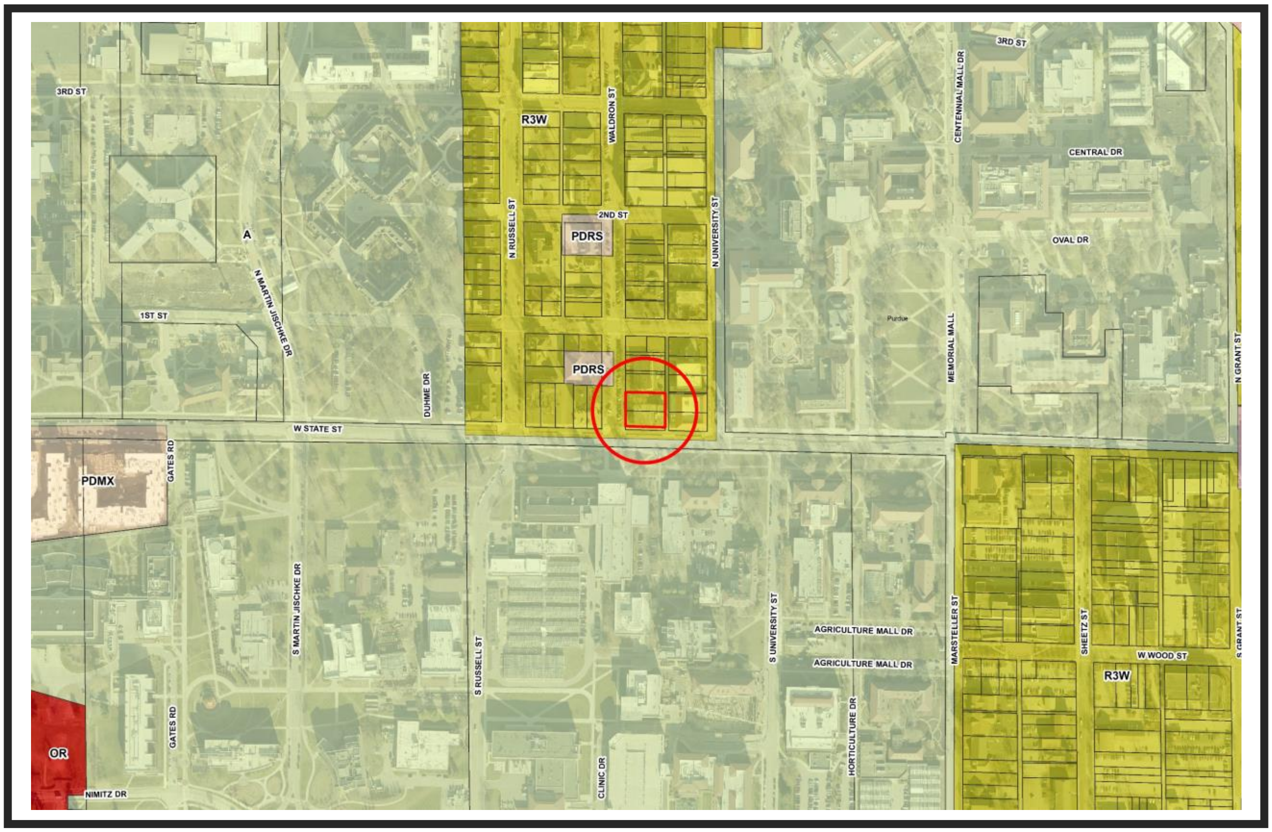

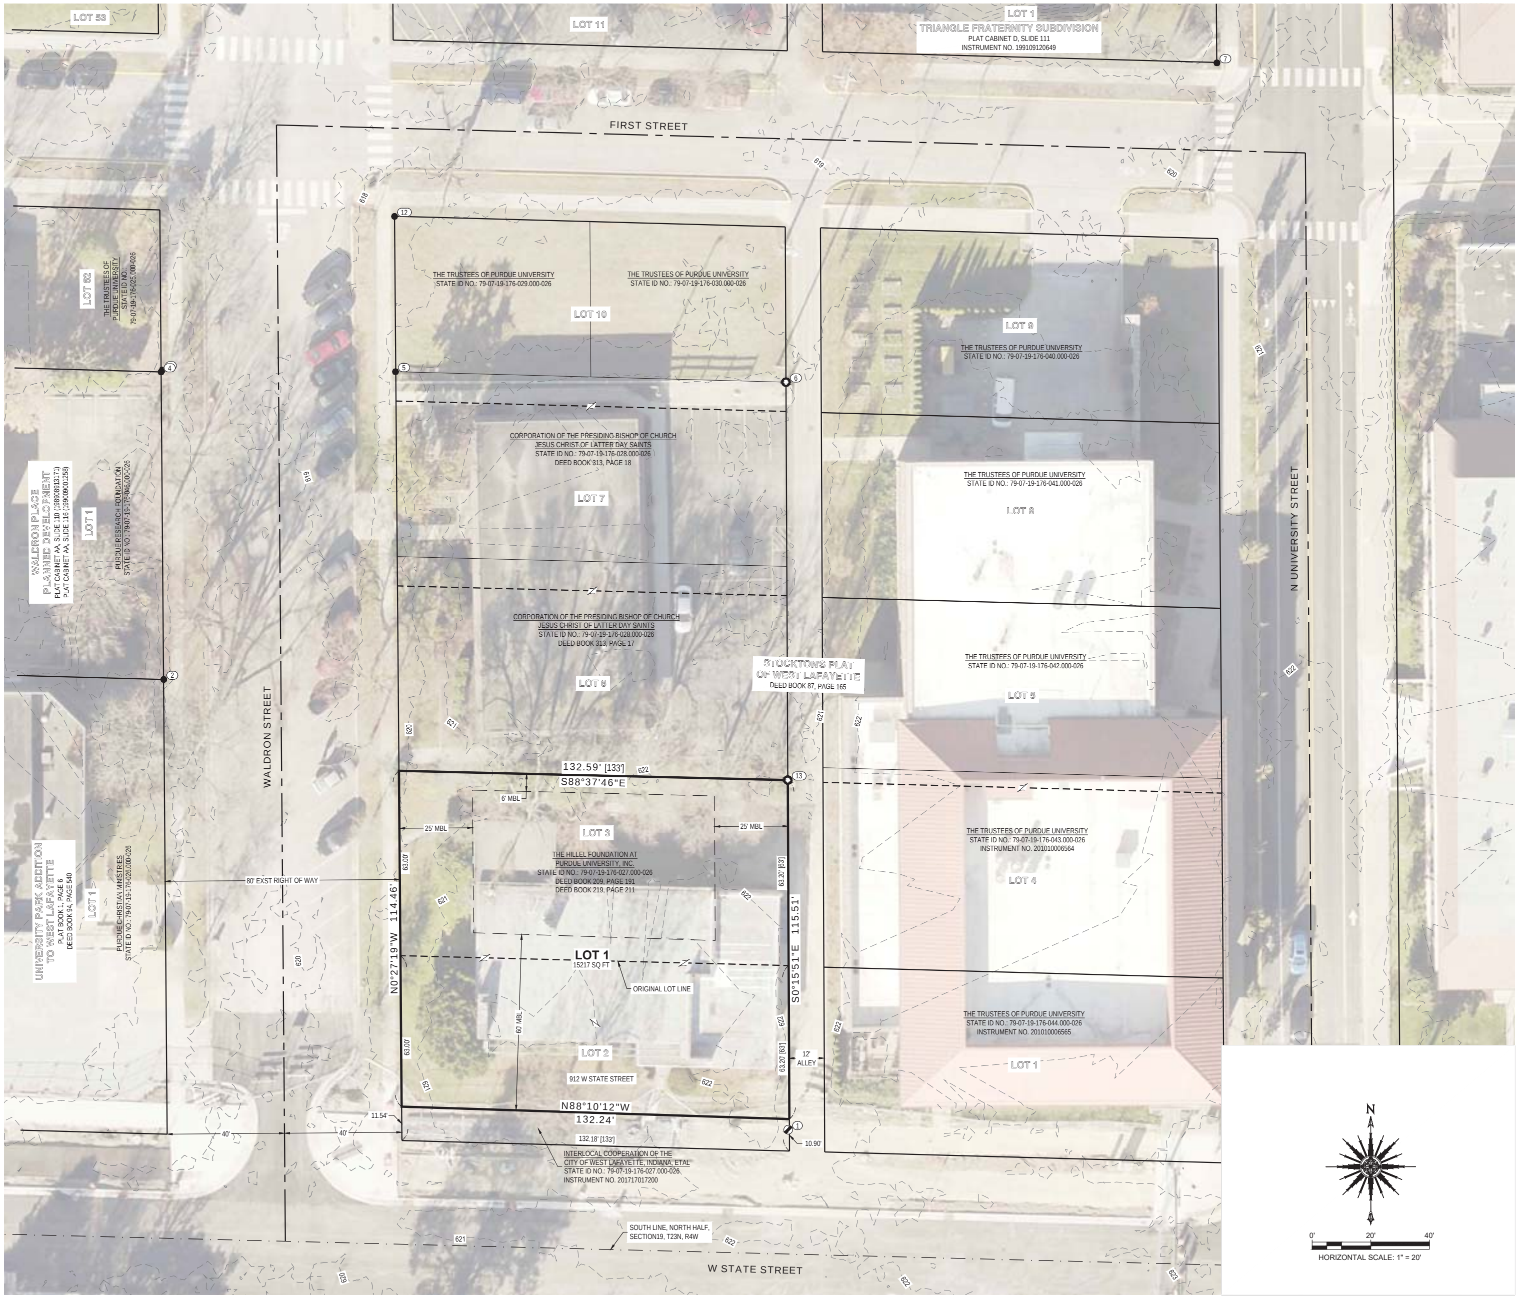
LOT 53
LOT 11
LOT 1
TRIANGLE FRATERNITY SUBDIVISION
PLAT CABINET D, SLIDE 111
INSTRUMENT NO. 199109120649
FIRST STREET
618
619
620
12
5
6
7
THE TRUSTEES OF PURDUE UNIVERSITY
STATE ID NO.: 79-07-19-176-029.000-026
THE TRUSTEES OF PURDUE UNIVERSITY
STATE ID NO.: 79-07-19-176-030.000-026
LOT 10
LOT 52
THE TRUSTEES OF PURDUE UNIVERSITY
STATE ID NO.: 79-07-19-176-025.000-026
4
CORPORATION OF THE PRESIDING BISHOP OF CHURCH
JESUS CHRIST OF LATTER DAY SAINTS
STATE ID NO.: 79-07-19-176-028.000-026
DEED BOOK 313, PAGE 18
LOT 7
CORPORATION OF THE PRESIDING BISHOP OF CHURCH
JESUS CHRIST OF LATTER DAY SAINTS
STATE ID NO.: 79-07-19-176-028.000-026
DEED BOOK 313, PAGE 17
LOT 6
WALDRON PLACE
PLANNED DEVELOPMENT
PLAT CABINET AA, SLIDE 110 (198908913171)
PLAT CABINET AA, SLIDE 116 (199009001258)
LOT 1
PURDUE RESEARCH FOUNDATION
STATE ID NO.: 79-07-19-176-046.000-026
2
WALDRON STREET
STOCKTON'S PLAT
OF WEST LAFAYETTE
DEED BOOK 87, PAGE 165
LOT 9
THE TRUSTEES OF PURDUE UNIVERSITY
STATE ID NO.: 79-07-19-176-040.000-026
THE TRUSTEES OF PURDUE UNIVERSITY
STATE ID NO.: 79-07-19-176-041.000-026
LOT 8
THE TRUSTEES OF PURDUE UNIVERSITY
STATE ID NO.: 79-07-19-176-042.000-026
LOT 5
N UNIVERSITY STREET
132.59' [133']
S88°37'46"E
13
6' MBL
25' MBL
25' MBL
LOT 3
THE HILLEL FOUNDATION AT
PURDUE UNIVERSITY, INC.
STATE ID NO.: 79-07-19-176-027.000-026
DEED BOOK 209, PAGE 191
DEED BOOK 219, PAGE 211
63.00'
63.00'
N0°27'19"W 114.46'
S0°15'51"E 115.51'
63.20' [63']
63.20' [63']
80' EXST RIGHT OF WAY
LOT 1
15217 SQ FT
ORIGINAL LOT LINE
60' MBL
LOT 2
912 W STATE STREET
12'
ALLEY
N88°10'12"W
132.24'
11.54'
10.90'
1
132.18' [133']
INTERLOCAL COOPERATION OF THE
CITY OF WEST LAFAYETTE, INDIANA, ETAL
STATE ID NO.: 79-07-19-176-027.000-026
INSTRUMENT NO. 201717017200
THE TRUSTEES OF PURDUE UNIVERSITY
STATE ID NO.: 79-07-19-176-043.000-026
INSTRUMENT NO. 201010006564
LOT 4
THE TRUSTEES OF PURDUE UNIVERSITY
STATE ID NO.: 79-07-19-176-044.000-026
INSTRUMENT NO. 201010006565
LOT 1
UNIVERSITY PARK ADDITION
TO WEST LAFAYETTE
PLAT BOOK 1, PAGE 6
DEED BOOK 94, PAGE 540
LOT 1
PURDUE CHRISTIAN MINISTRIES
STATE ID NO.: 79-07-19-176-026.000-026
SOUTH LINE, NORTH HALF,
SECTION19, T23N, R4W
W STATE STREET
621
622
N
0'
20'
40'
HORIZONTAL SCALE: 1" = 20'

SKETCH PLAN

PURDUE-HILLEL MINOR SUBDIVISION

A REPLAT OF LOT 2 & 3 IN
STOCKTONS ADDITION TO WEST LAFAYETTE
A PART OF THE NORTHWEST QUARTER OF SECTION 19,
TOWNSHIP 23 NORTH, RANGE 4 WEST,
WABASH TOWNSHIP, TIPPECANOE COUNTY, INDIANA

RECORD LEGAL DESCRIPTION(S)

The West half of Lots numbered two (2) and three (3) in Stockton's Plat of West Lafayette, as platted upon part of the East half of the North-west quarter of Section nineteen (19), in Township twenty-three (23) North, Range four (4) West, lying west of and adjoining the Purdue University Grounds. Located in Wabash Township, Tippecanoe County, Indiana

ALSO Sixty-six and one-half (66 $\frac{1}{2}$) feet of even width off of the entire East side of Lots numbered two (2) and three (3) in Stockton's Plat of West Lafayette, as platted upon part of the East half of the North-west quarter of Section nineteen (19), in Township twenty-three (23) North, Range four (4) West, lying west of and adjoining the Purdue University Grounds. Located in Wabash Township, Tippecanoe County, Indiana.

EXCEPT the Interlocal Cooperation Board of the City of West Lafayette, Indiana, etal real estate as described in Instrument Number 201717017200 in the Office of the Tippecanoe County Recorder, described as follows:

A part of Lot 2 in the Stockton's Plat of the City of West Lafayette, Indiana, the plat of which is recorded in Deed Record 87, page 165, in the Office of the Recorder of Tippecanoe County, Indiana, and being that part of the grantor's land lying within the right-of-way lines depicted on the attached Right-of-Way Parcel Plat, marked Exhibit "B", described as follows: Beginning at the southwest corner of said lot; thence North 0 degrees 25 minutes 41 seconds West 11.54 feet along the west line of said lot to point "1198" designated on said plat; thence South 88 degrees 26 minutes 50 seconds East 134.25 feet to a point "1199" designated on said plat on the east line of said lot; thence South 0 degrees 15 minutes 30 seconds East 10.90 feet along said east line to the southeast corner of said lot; thence North 88 degrees 43 minutes 21 seconds West 134.20 feet (133 feet by said Deed Record 87, page 165) along the south line of said lot to the point of beginning and containing 1,505 square feet, more or less.

LAST INSTRUMENT CONVEYING TITLE TO SUBJECT PROPERTY:

STATE ID NO:	79-07-19-176-027.000-026
DEED RECORD:	DEED BOOK 209, PAGE 191
GRANTOR:	LOUIS & BEATRICE PEARLMAN
GRANTEE:	INDIANA B'NAI B'RITH HILLEL FOUNDATION, INC.
DATE:	OCTOBER 10, 1946
STATE ID NO:	79-07-19-176-027.000-026
DEED RECORD:	DEED BOOK 219, PAGE 211
GRANTOR:	THE PURDUE CHAPTER OF TAU EPSILON PHI, INCORPORATED
GRANTEE:	INDIANA B'NAI BRITH HILLEL FOUNDATION, INC.
DATE:	JANUARY 31, 1949

NOTE: SEE AFFIDAVIT OF TITLE AND ADVERSE POSSESSION, INSTRUMENT NO. 200606006712 FOR ADDITIONAL INFORMATION PERTAINING TO CURRENT TITLE.

LAND SURVEYOR'S CERTIFICATE

The undersigned, a Registered Professional Land Surveyor of the State of Indiana does hereby certify that the above sketch plan or preliminary plat was prepared under his direct supervision.

CERTIFIED BY:

P. Will 05/20/2019
Patrick E. Williams, PLS Date

SURVEY NOTE

This drawing does not represent a boundary survey of the property depicted and is based on a boundary survey of the subject property prepared by TBIRD Design Services Corp., Project No. 19031. This plat has been prepared pursuant to Section 3.4 (Minor Subdivisions) and Sections 6.1 & 6.2 (Sketch Plan & Preliminary Plat), of the Unified Subdivision Ordinance of Tippecanoe County as amended November, 1988.

UTILITY SERVICE NOTE

The subject real estate appears to be serviced by existing water and sanitary sewer facilities located within adjacent public right of way.

LEGEND

– – – – – – – – (light)	= EXISTING EASEMENT AS NOTED
—— —— —— ——	= PROPOSED BUILDING SETBACK
– – – – – – – –	= PROPOSED EASEMENT AS NOTED
MBL	= MINIMUM BUILDING SETBACK LINE
——W——	= EXISTING WATER
——SS——	= EXISTING SANITARY SEWER
——ST——	= EXISTING STORM SEWER

MONUMENT TABLE

POINT #	NORTHING	EASTING	ELEV	DESCRIPTION
1	1885292.57	2998979.68	621.86	CROSS CUT-X FOUND IN SIDEWALK
2	1885446.00	2998766.82	620.33	REBAR W/ RWG CAP FOUND -0.1' BELOW GRADE
3	1885551.48	2998766.36	619.65	REBAR W/ LS 1244 CAP FOUND AT GRADE
4	1885550.80	2998765.92	619.63	REBAR W/ RWG CAP FOUND AT GRADE
5	1885550.89	2998845.81	619.29	REBAR W/ SCHNEIDER CAP FOUND AT GRADE
6	1885547.32	2998978.92	621.95	1" IRON PIPE FOUND +0.75' ABOVE GRADE
7	1885656.12	2999125.84	620.35	REBAR W/ VESTER CAP FOUND -0.5' BELOW GRADE
11	1885720.90	2998979.09	619.14	RAILROAD SPIKE FOUND -0.2' BELOW GRADE
12	1885603.80	2998845.48	618.08	BENT 5/8" REBAR FOUND -0.5' BELOW GRADE
13	1885411.72	2998979.54	620.58	1 1/2" IRON PIPE FOUND -1.1' BELOW GRADE
14	1885167.76	3002231.29	584.02	SECTION CORNER
15	1885300.08	2997013.54	627.12	SECTION CORNER

TBIRD
Design Services Corporation
Engineering • Surveying
Environmental • Construction Management
105 North 10th Street • Lafayette, Indiana
(765) 742-1900 • info@tbirddesign.com
www.tbirddesign.com

CERTIFIED BY:

PATRICK E. WILLIAMS
REGISTERED
NO. 20800122
STATE OF INDIANA
LAND SURVEYOR

P. Will

HILLEL FOUNDATION
AT PURDUE UNIVERSITY, INC.
912 STATE STREET
WEST LAFAYETTE, IN 47906

KJG ARCHITECTURE
527 SAGAMORE PKWY W, STE 101 WEST
WEST LAFAYETTE, IN 47906

MARK	DATE	DESCRIPTION

PROJECT NO:	19031
FILE:	19031-SKETCH PLAN.DWG
DRAWN BY:	MBH
CHECKED BY:	PEW

LOCATION:

A PART OF THE NORTHWEST QUARTER
OF SECTION 19, TOWNSHIP 23 NORTH,
RANGE 4 WEST, WABASH TOWNSHIP,
TIPPECANOE COUNTY, INDIANA

TITLE:

SKETCH PLAN

V101
1 OF 1

FILE: P:\2019\19031 Hillel Foundation at Purdue -Minor\DRAWINGS\SURVEY\19031-SKETCH PLAN.dwg - USER: PATRICK WILLIAMS - DATE: Monday, May 20, 2019 2:37:05 PM

S-4850
PURDUE-HILLEL MINOR SUBDIVISION
A replat of Lots 2 & 3 in Stockton's Addition to West Lafayette
Minor-Sketch Plan

Staff Report
June 13, 2019

REQUEST MADE, PROPOSED USE, LOCATION:

Petitioner and owner, the Hillel Foundation at Purdue University, Inc. by Philip Schlossberg, represented by Patrick Williams of TBird Design Services Corporation, is seeking primary approval to replat two lots into one, on 0.35 acres, located on the northeast corner of State and Waldron Streets, West Lafayette, Wabash 19 (NW) 23-4. Petitioner is planning to expand the existing building which currently crosses the platted lot line.

AREA ZONING PATTERNS:

The lots are zoned R3W as are the lots adjacent to the east, north and west. A few properties zoned PDRS are scattered throughout this area commonly called “the island” (the three blocks in the city surrounded by Purdue’s campus formerly outside of the city limits; the city annexed Purdue’s campus in 2014.) Land across State Street to the south is Purdue-owned and zoned Agricultural.

AREA LAND USE PATTERNS:

The area is a mix of campus buildings and religious organizations catering to the student population. On site, the Hillel Foundation provides religious services and more to Purdue’s Jewish students.

TRAFFIC AND TRANSPORTATION:

The site is on the northeast corner of State and Waldron Streets. State is classified as a primary arterial by the adopted *Thoroughfare Plan*. The required half-width right-of-way is already in place; an 11’ wide strip was dedicated as part of the Re-State road project. Waldron Street is a local and again, the required right-of-way already exists. So, no further dedication or mortgage release is necessary. The driveway currently serving the property is off the north-south running alley to the east. The building addition plans show no changes to this existing sole access.

ENVIRONMENTAL AND UTILITY CONSIDERATIONS:

Public utilities currently serve the site.

CONFORMANCE WITH UZO REQUIREMENTS:

Variance requests have been filed for this site, originally to be heard at the June ABZA meeting; however, petitioner has requested a continuance to the July meeting in order to add another variance request. Currently the requests include: a reduction in the required parking spaces; an increase in the building lot coverage percentage and two setback variances. The setback requests are a 16’ setback from Waldron Street instead of 25’ and a rear setback of 6’ instead of the minimum setback of 25’. The additional setback would vary the front setback from State Street. If these setback variances are approved, they will need to be shown and noted on the final plat.

Lot width and area meets the ordinance standards for the R3W zone.

STAFF RECOMMENDATION:
Conditional primary approval, contingent on the following:

A. Conditions

FINAL PLAT – The following items shall be part of the Secondary Application and Final Plat approval:

1. All existing easements, covenants or restrictions shall be shown and referenced with the corresponding recording information (Document Number and date recorded).

2. All required building setbacks (per the action of the ABZA) shall be platted.

3. The street addresses and County Auditor's Key Number shall be shown.