

# S-4749
# WEST LAFAYETTE HIGH SCHOOL MINOR SUBDIVISION, A REPLAT OF LOTS 1-36, CHARLES W. ROSS ADDITION, PLUS UNPLATTED LAND
## (minor-sketch)

## STAFF REPORT
## May 10, 2018

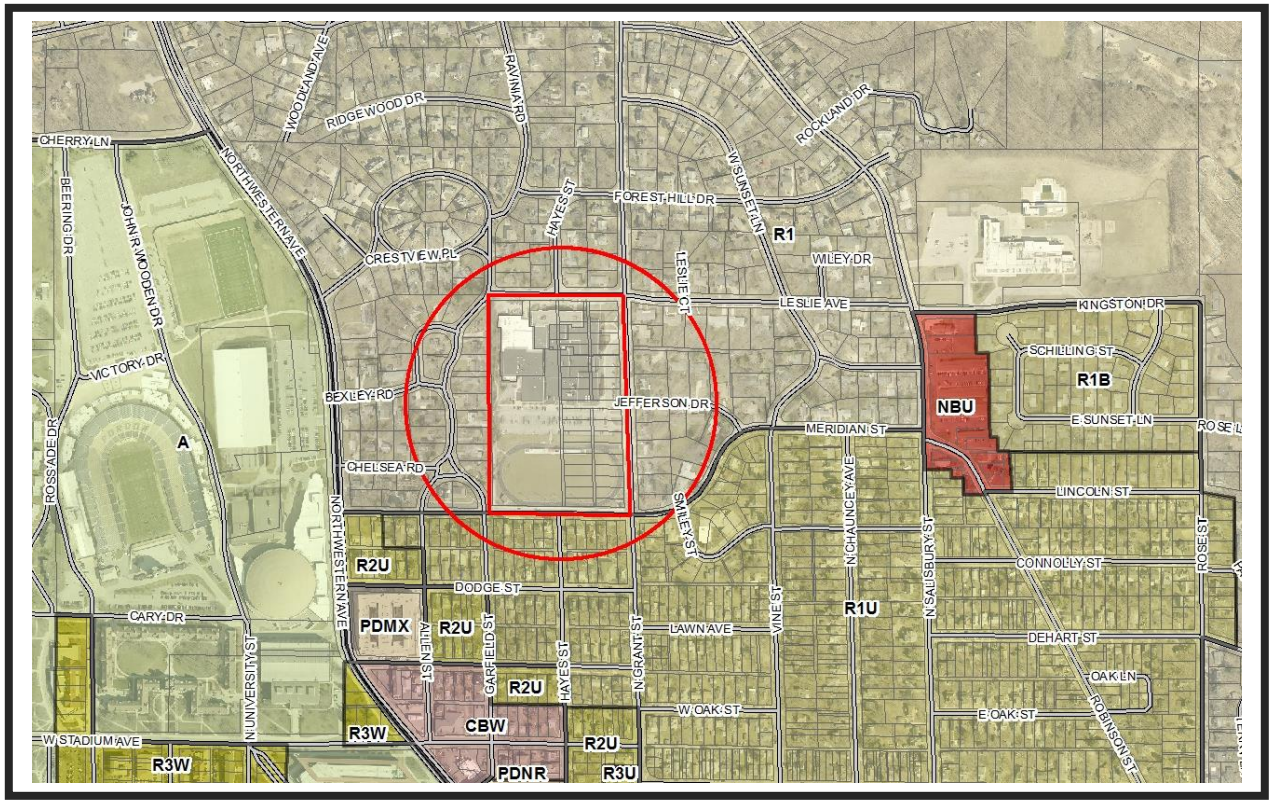

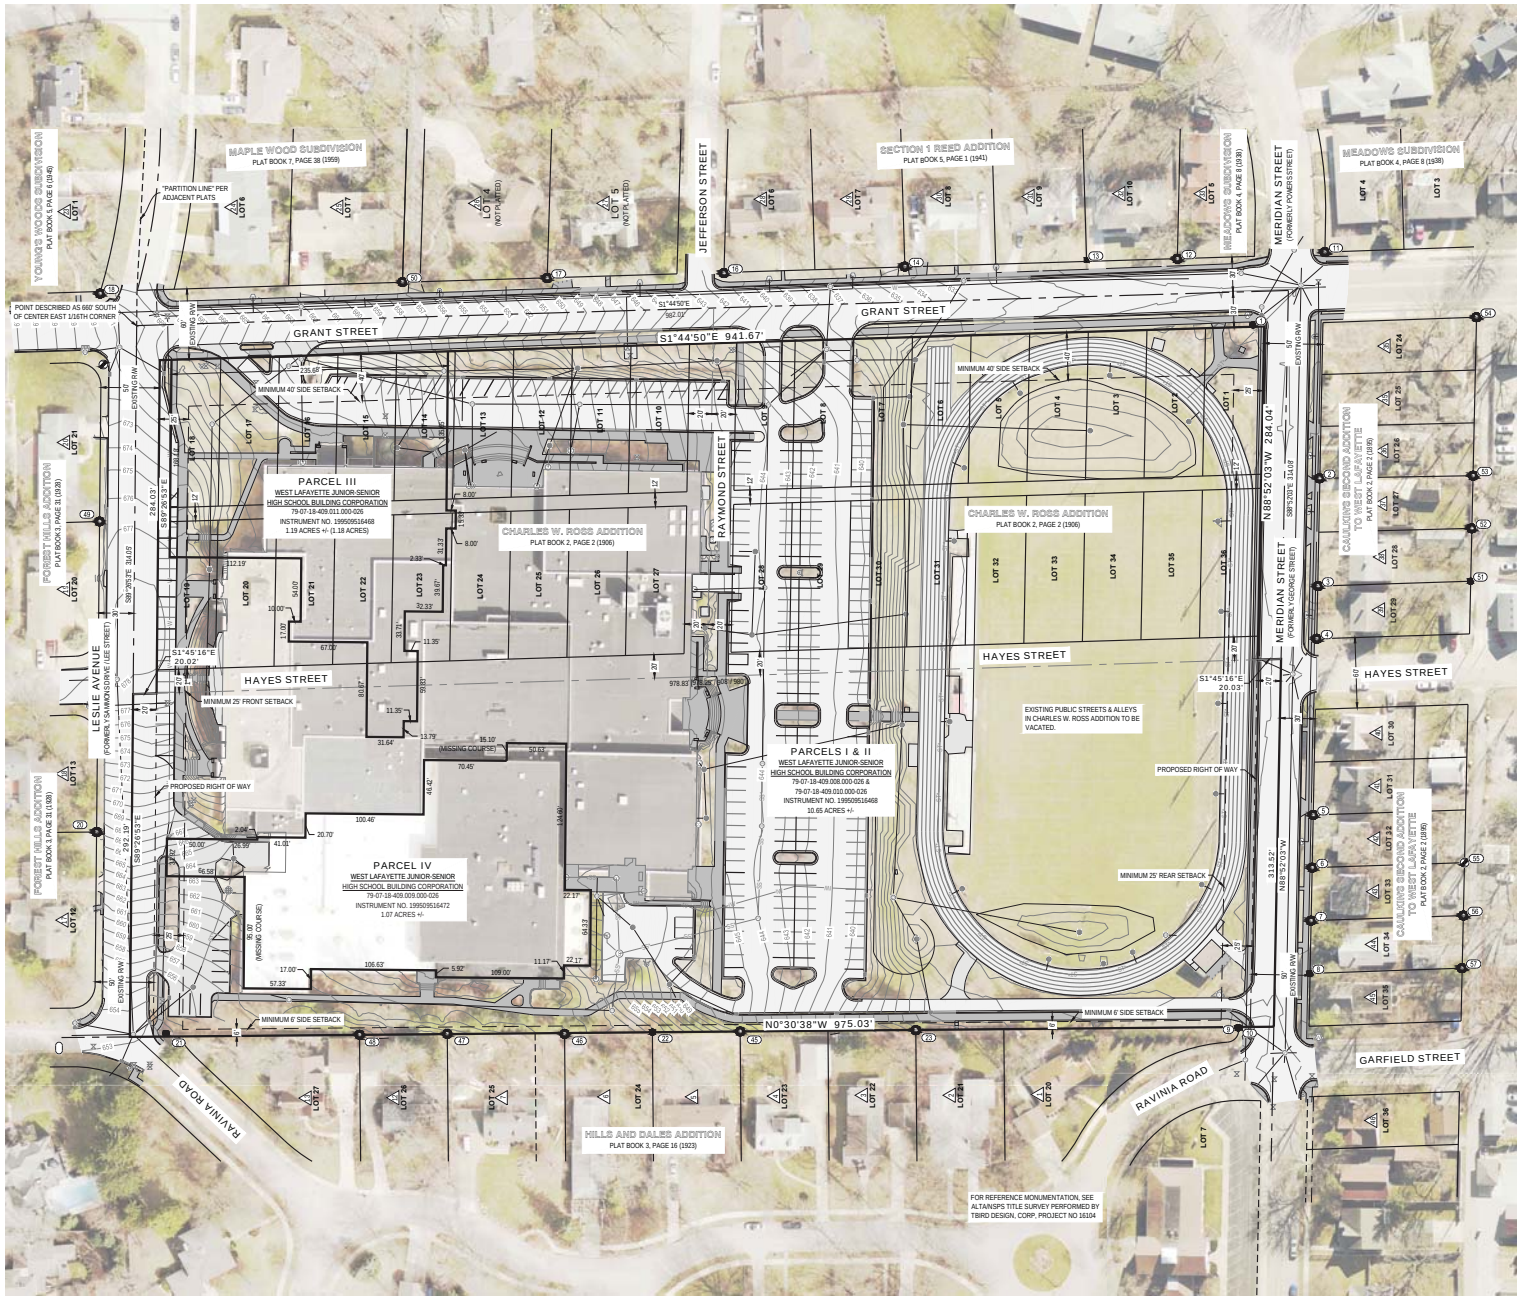


## ADJOINER TABLE

| ID | OWNER | STATE ID | INSTRUMENT NUMBER |
|---|---|---|---|
| 1 | MCCALLUM, JANET R AS TRUSTEE | 79-07-18-454-001.000-026 | 201010000267 |
| 2 | BEHM, STEPHEN J & HARRIETT L | 79-07-18-454-002.000-026 | 200404003937 |
| 3 | MILAM, ANDREW D & TWYLA | 79-07-18-409-001.000-026 | 201313011156 |
| 4 | PINAL, RODOLFO & CARVAJAL TERESA | 79-07-18-409-002.000-026 | 200303004898 |
| 5 | EAGON, JOHN C & JANE M | 79-07-18-409-003.000-026 | 201717006202 |
| 6 | GLEICH, DAVID F & BOFFERDING LAURA | 79-07-18-409-004.000-026 | 201212012609 |
| 7 | BERGER, EDWARD J & CARRIE A | 79-07-18-409-005.000-026 | 201414017334 |
| 12 | WEBB, CHRISTOPHER S & DENISE M | 79-07-18-409-006.000-026 | 201515008060 |
| 13 | SHIVELY, GERALD E & MONICA M | 79-07-18-409-007.000-026 | 200606021062 |
| 17 | SCHMIERER, JEFFREY D & KIMBERLY MARIE | 79-07-18-404-004.000-026 | 199709715025 |
| 18 | JOHNSON, CHARLES R JR & SARAH E. GUERRETTAZ | 79-07-18-404-003.000-026 | 200101014138 |
| 19 | WULLE, BERNARD W | 79-07-18-403-006.000-026 | 200404020048 |
| 20 | LUCAS, ERIC M | 79-07-18-403-005.000-026 | 201616012632 |
| 23 | HERTEL, THOMAS W & ADRIELA FERNANDEZ | 79-07-18-429-007.000-026 | 199509510838 |
| 24 | CHANDRASEKAR, SRINIVASAN & VEDA | 79-07-18-432-004.000-026 | 199409418490 |
| 25 | ALLINGTON, JOHN T | 79-07-18-432-003.000-026 | 201313020376 |
| 26 | DURAI, MELVIN S. & MALATHI RAGHAVAN | 79-07-18-432-002.000-026 | 201717014069 |
| 27 | VOLKMAN, TIMOTHY J & BEVERLY B | 79-07-18-432-001.000-026 | DEED BOOK 316, PAGE 399 |
| 28 | IVANTYSYN, ROMAN | 79-07-18-431-002.000-026 | 201010009568 |
| 29 | WOOD, RANDALL & KIMBERLY R. | 79-07-18-431-001.000-026 | 201717015291 |
| 30 | WILCOX, PHILIP & NANCY | 79-07-18-476-003.000-026 | 200909014428 |
| 31 | NOUR, ABDELFATTAH Y.M. & SULMA I. MOHAMMED | 79-07-18-476-002.000-026 | 199309303718 |
| 32 | NAIMI, LINDA TRUSTEE | 79-07-18-476-001.000-026 | 201313020465 |
| 33 | JONES, BRIAN K | 79-07-18-476-007.000-026 | 200806009447 |
| 35 | BANKS, JO ANN | 79-07-18-455-001.000-026 | 199209204614 |
| 36 | DWK DENTAL EQUITY HOLDINGS LLC | 79-07-18-455-002.000-026 | 201515019416 |
| 37 | LAMBRIGHT, COLETTE E. & KURT M. | 79-07-18-455-003.000-026 | 201313024258 |
| 38 | SCHWEITZER, LEE E. | 79-07-18-455-004.000-026 | 199008001465 |
| 39 | WEIDA HOLDINGS LLC | 79-07-18-455-005.000-026 | 201616024089 |
| 40 | JE LIMITED PARNERSHIP | 79-07-18-456-001.000-026 | 199709723950 |
| 41 | FOERG, PATRICIA L. | 79-07-18-456-003.000-026 | 198808808014 |
| 42 | SCHROEDER, GARY W. | 79-07-18-456-004.000-026 | 200808023863 |
| 43 | SCHROEDER, GARY W. | 79-07-18-455-005.000-026 | 201717013802 |
| 44 | VOLKMAN, BEVERLY B | 79-07-18-456-006.000-026 | PRIOR CONVEYANCE DEED BOOK 279, PAGE 135 |
| 45 | WEIDA, JERRY M. & DANIELLE P. | 79-07-18-456-007.000-026 | 201212001635 |
| 46 | SAWYER, CHARLES J. & BEVERLY E. AS TRUSTEES | 79-07-18-457-001.000-026 | 200505020648 |


TBIRD
Design Services Corporation
Engineering • Surveying
Environmental • Construction Management
105 North 13th Street • Lafayette, Indiana 47904
(765) 742-1361 • Fax (765) 742-1369
www.tbirddesign.com


CERTIFIED BY:

PATRICK E. WILLIAMS
REGISTERED
NO 20600122
STATE OF INDIANA
LAND SURVEYOR

WEST LAFAYETTE JUNIOR-SENIOR HIGH SCHOOL SUBDIVISION
WEST LAFAYETTE JUNIOR-SENIOR HIGH SCHOOL BUILDING CORPORATION
P.O. BOX 1535
LAFAYETTE, IN 47902


| MARK | DATE | DESCRIPTION |
|---|---|---|

PROJECT NO: 16104
FILE: 16104-SKETCH PLAN.DWG
DRAWN BY: CDB
CHECKED BY: PEW
LOCATION:
A PART OF THE SOUTHEAST QUARTER OF SECTION 18, TOWNSHIP 23 NORTH, RANGE 4 WEST, WABASH TOWNSHIP, TIPPECANOE COUNTY, INDIANA

TITLE:
DRAFT PLAN
SITE ANALYSIS

1
1 OF 2


FILE: P:\2016\16104 West Lafayette High School\DWG\SURVEY\PLAN\16104-SKETCH PLAN.dwg USER: PATRICK WILLIAMS DATE: Friday, April 13, 2018 12:21:53 PM

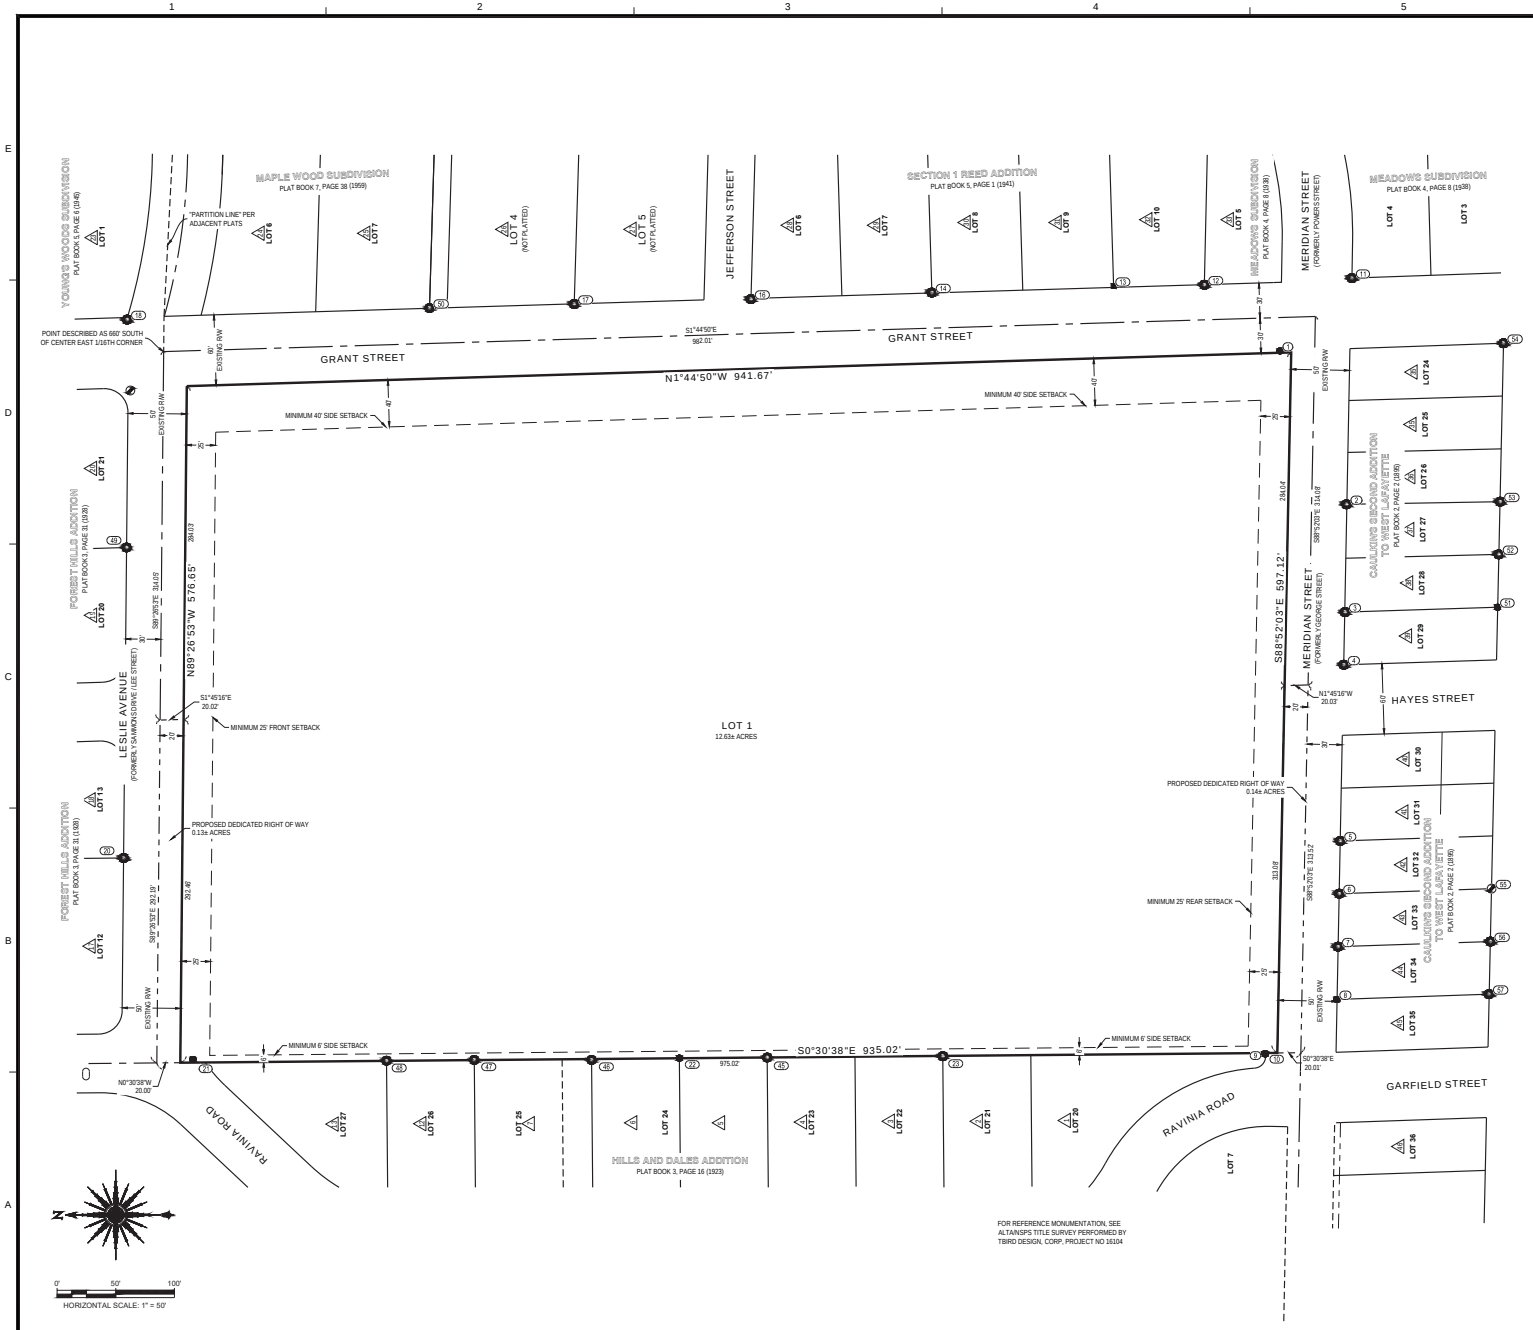


# WEST LAFAYETTE JUNIOR-SENIOR HIGH SCHOOL SUBDIVISION

SOUTHEAST QUARTER OF SECTION 18, TOWNSHIP 23 NORTH, RANGE 4 WEST, WABASH TOWNSHIP, TIPPECANOE COUNTY, INDIANA

CORRECTED RECORD LEGAL DESCRIPTION - PARCELS I, II, AND III

A part of the west half of the southeast quarter of Section Eighteen (18), Township twenty-three (23) North, Range Four (4) West, described as follows:

Commencing at a point on the east line of the above described west half of the southeast quarter six hundred sixty (660) feet south of the northeast corner thereof, said point being in the center of the public thorofare known as Grant Street, and running thence south with said centerline and with the east line of the tract nine hundred eighty-one (981) feet to a point in said Grant Street common to the north line of Caulkins Second Addition; thence west with said north line and along the line of Meridian Street three hundred fifteen (315) feet; thence northward nine hundred seventy-eight and one-fourth (978 1/4) feet; thence east three hundred two (302) feet to place of beginning, containing seven (7) acres, more or less. EXCEPT therefrom a tract of land one hundred (100) feet wide north and south by one hundred fifty (150) feet long out of the southeast corner thereof and which last described tract is known as Lots No. one (1) and two (2) in C.W. Ross' Addition to West Lafayette, Indiana. The tract above described includes Lots numbered three (3) to thirty-six (36), inclusive, in the C.W. Ross' Addition to West Lafayette, Indiana, which is the whole of said addition except Lots 1 and 2 thereof. Also all streets and alleys as laid out in said Addition.

ALSO, Lots numbered One (1) and Two (2) in Charles W. Ross' Addition to the town, now city of West Lafayette, Indiana, consisting of a tract of land one hundred (100) feet wide north and south by one hundred fifty (150) feet long out of the southeast corner of the following described tract, to-wit:

A part of the west half of the southeast quarter of Section Eighteen (18), Township Twenty-three (23) North, Range Four (4) West, described as follows: Commencing at a point on the East line of the above described west half of the southeast quarter six hundred sixty (660) feet south of the northeast corner thereof, said point being in the center of the public thorofare known as Grant Street, and running thence south with said centerline and with the east line of the tract nine hundred eighty-one (981) feet to a point in said Grant Street common to the north line of Caulkins Second Addition; thence West with said north line and along the line of Meridian Street three hundred fifteen (315) feet; thence northward nine hundred seventy-eight and one-fourth (978 1/4) feet; thence east three hundred two (302) feet to place of beginning, containing seven and 20/100 (7.20) acres, more or less.

ALSO, The west half of the east half of the following described tract:

A part of the west half of the southeast quarter of Section Eighteen (18) in Township Twenty-three (23) North, Range Four (4) West, beginning at a point on the west line of said quarter section forty (40) rods south of the northwest corner thereof, and running due east parallel with the north line of said tract eighty (80) rods to the east line of said tract; thence south on said east line seventy-nine and 4/100 (79.04) rods; thence west eighty (80) rods to the west line of said quarter section; thence north seventy-nine and 4/100 (79.04) rods to the place of beginning. EXCEPT therefrom a strip off of and from the entire south side of said tract three hundred thirty-five (335) feet in width north and south being that part of said section platted into town lots and known as Caulkin's First and Second Additions to the town, now City of West Lafayette, Indiana.

EXCEPTING THEREFROM Land in Tippecanoe County, Indiana, being part of the west half of the southeast quarter of Section 18, Township 23 North, Range 4 West, more particularly described as follows:

Commencing at the northeast corner of the west half of the southeast quarter of said Section 18, run South along said half quarter section line and centerline of Grant Street a distance of 660.00 feet to a point at the intersection of the centerline of Leslie Avenue and Grant Street; thence deflecting 91 degrees 30 minutes right a distance of 468.96 feet along the centerline of Leslie Avenue to a point; thence deflecting 90 degrees left a distance of 30.00 feet to the point of beginning; thence continuing on the last above course a distance of 66.58 feet to a point; thence deflecting 90 degrees right 95.00 feet to a point; thence deflecting 90 degrees left 57.33 feet to a point; thence deflecting 90 degrees left 17.00 feet to a point; thence deflecting 90 degrees right 106.93 feet to a point; thence deflecting 90 degrees right 5.92 feet to a point; thence deflecting 90 degrees left 109.00 feet to a point; thence deflecting 90 degrees left 11.17 feet to a point; thence deflecting 90 degrees right 22.17 feet to a point; thence deflecting 90 degrees left 64.33 feet to a point; thence deflecting 90 degrees left 22.17 feet to a point; thence deflecting 90 degrees right 124.60 feet to a point; against the west wall near the southwest corner of the existing auditorium unit of the existing building; thence deflecting 90 degrees left along the existing building wall a distance of 50.63 feet to a point; thence deflecting 90 degrees left 15.10 feet to a point; thence deflecting 90 degrees right 70.45 feet to a point; thence deflecting 90 degrees left 46.42 feet to a point; thence deflecting 90 degrees right 100.46 feet to a point; thence deflecting 90 degrees left 20.70 feet to a point; thence deflecting 90 degrees right 41.01 feet to a point; thence deflecting 90 degrees left 2.04 feet to a point; thence deflecting 90 degrees right 26.99 feet to a point which is the northwest corner of the existing building; and continuing on the last above course 50.00 feet to a point; thence deflecting 90 degrees left 31.92 feet to the point of beginning, containing 1.07 acres.

CORRECTED RECORD LEGAL DESCRIPTION - PARCELS IV

Land in Tippecanoe County, Indiana being part of the west half of the southeast quarter of Section 18, Township 23 North, Range 4 West, more particularly described as follows:

Commencing at the northeast corner of the west half of the southeast quarter of said Section 18, run South along said half quarter section line and centerline of Grant Street a distance of 660.00 feet to a point at the intersection of the centerline of Leslie Avenue and Grant Street; thence deflecting 91 degrees 30 minutes right a distance of 468.96 feet along the centerline of Leslie Avenue to a point; thence deflecting 90 degrees left a distance of 30.00 feet to the point of beginning; thence continuing on the last above course a distance of 66.58 feet to a point; thence deflecting 90 degrees right 95.00 feet to a point; thence deflecting 90 degrees left 57.33 feet to a point; thence deflecting 90 degrees left 17.00 feet to a point; thence deflecting 90 degrees right 106.93 feet to a point; thence deflecting 90 degrees right 5.92 feet to a point; thence deflecting 90 degrees left 109.00 feet to a point; thence deflecting 90 degrees left 11.17 feet to a point; thence deflecting 90 degrees right 22.17 feet to a point; thence deflecting 90 degrees left 64.33 feet to a point; thence deflecting 90 degrees left 22.17 feet to a point; thence deflecting 90 degrees right 124.60 feet to a point; against the west wall near the southwest corner of the existing auditorium unit of the existing building; thence deflecting 90 degrees left along the existing building wall a distance of 50.63 feet to a point; thence deflecting 90 degrees left 15.10 feet to a point; thence deflecting 90 degrees right 70.45 feet to a point; thence deflecting 90 degrees left 46.42 feet to a point; thence deflecting 90 degrees right 100.46 feet to a point; thence deflecting 90 degrees left 20.70 feet to a point; thence deflecting 90 degrees right 41.01 feet to a point; thence deflecting 90 degrees left 2.04 feet to a point; thence deflecting 90 degrees right 26.99 feet to a point which is the northwest corner of the existing building; and continuing on the last above course 50.00 feet to a point; thence deflecting 90 degrees left 31.92 feet to the point of beginning, containing 1.07 acres.

## LAST INSTRUMENT CONVEYING TITLE TO SUBJECT PROPERTY:

| | |
|---|---|
| STATE ID NO: | 79-07-18-409.008.000-026 & 79-07-18-409.010.000-026 79-07-18-409.011.000-026 |
| INSTRUMENT NO: | 199509516468 |
| GRANTOR: | WEST LAFAYETTE COMMUNITY SCHOOL CORPORATION |
| GRANTEE: | WEST LAFAYETTE JUNIOR-SENIOR HIGH SCHOOL BUILDING CORPORATION |
| DATE: | SEPTEMBER 27, 1995 |
| STATE ID NO: | 79-07-18-409.009.000-026 |
| INSTRUMENT NO: | 199509516472 |
| GRANTOR: | PHASE THREE HIGH SCHOOL BUILDING CORPORATION |
| GRANTEE: | WEST LAFAYETTE JUNIOR-SENIOR HIGH SCHOOL BUILDING CORPORATION |
| DATE: | SEPTEMBER 27, 1995 |

## LAND SURVEYOR'S CERTIFICATE

The undersigned, a Registered Professional Land Surveyor of the State of Indiana does hereby certify that the above preliminary plat was prepared under his direct supervision.

CERTIFIED BY:

04/13/2018

Patrick E. Williams, PLS — Date

## SURVEY NOTE

This drawing does not represent a boundary survey of the property and is based on a previous boundary survey of the subject property prepared by TBIRD Design Services Corp Job No. 16104. This plat has been prepared pursuant to Section 3.4 (Minor Subdivisions) and Sections 6.1 & 6.2 (Sketch Plan & Preliminary Plat), of the Unified Subdivision Ordinance of Tippecanoe County as amended November, 1988


TBIRD
Design Services Corporation
Engineering • Surveying
Environmental • Construction Management
105 North 13th Street • Lafayette, Indiana
(765) 742-1964 • www.tbirddesign.com


CERTIFIED BY:

PATRICK E. WILLIAMS — REGISTERED — NO 20600122 — STATE OF INDIANA — LAND SURVEYOR

WEST LAFAYETTE JUNIOR-SENIOR HIGH SCHOOL SUBDIVISION
WEST LAFAYETTE JUNIOR-SENIOR HIGH SCHOOL BUILDING CORPORATION
P.O. BOX 1535
LAFAYETTE, IN 47902

| NO | DATE | DESCRIPTION |
|---|---|---|

| | |
|---|---|
| PROJECT NO: | 16104 |
| FILE: | 16104-SKETCH PLAN.DWG |
| DRAWN BY: | CDB |
| CHECKED BY: | PEW |

LOCATION:

A PART OF THE SOUTHEAST QUARTER OF SECTION 18, TOWNSHIP 23 NORTH, RANGE 4 WEST, WABASH TOWNSHIP, TIPPECANOE COUNTY, INDIANA

TITLE:

SKETCH PLAN

GEOMETRICS

2

2 OF 2


FILE: P:\2016\16104 West Lafayette High School\DRAWINGS\PLANS\DWG\PT PLAN\16104-SKETCH PLAN.dwg USER: PATRICK WILLIAMS DATE: Friday, April 13, 2018 1:22:16 PM

# S-4749
# WEST LAFAYETTE HIGH SCHOOL MINOR SUBDIVISION
# Minor-Sketch Plan

**Staff Report**
**May 10, 2018**

**REQUEST MADE, PROPOSED USE, LOCATION:**
Petitioner, West Lafayette Junior-Senior High School Building Corporation (represented by attorney Kevin Riley of Reiling Teder & Schrier LLC and surveyor Patrick Williams of TBIRD Design Services) is seeking primary approval to combine several lots and unplatted land into a single lot on 12.91 acres, located on the west side of Grant Street, between Leslie Avenue and Meridian Street, in West Lafayette, Wabash 18(SE)23-4.

**AREA ZONING PATTERNS:**
The site is zoned R1 (Single-family Residential) and is part of a large R1 district north of Meridian Street. South of Meridian Street is a large R1U (Single-family Residential Urban) area.

**AREA LAND USE PATTERNS:**
The north half of the site is occupied by the West Lafayette Junior / Senior High School building and the parking lot, running track and football field are located on the south half. Underlying the east half of the school property are the 36 lots of the Charles W. Ross Addition. The west half of the site was never platted. Except for two neighborhood churches near the south end, the surrounding area land use is predominantly single-family residential.

**TRAFFIC AND TRANSPORTATION:**
Leslie Avenue is classified as an urban local road and will have the total required right-of-way of 50-ft after dedication of a 20-ft wide strip of land on the final plat. Because Grant and Meridian Streets are classified by the *Thoroughfare Plan* as urban secondary arterials, they are both required to have half-width rights-of-way of 35-ft. The existing half-width right-of-way for Grant Street is 30-ft (requiring 5 more feet). Most of a 50-ft wide full right-of-way is in place for Meridian Street, which has an offset centerline (20-ft on the north side and 30-ft on the south). The sketch plan shows a planned dedication of 20-ft to complete the 50-ft wide right-of-way along the full frontage. However to comply with the urban secondary arterial standard, an additional 10-ft would need to be dedicated along the north side of Meridian. Variances have been requested with this subdivision application to waive the required secondary arterial right-of-way dedication. Both Grant and Meridian Streets fully occupy the existing rights-of-way. Dedicating the additional right-of-way would place the existing running tract inside public street right-of-way along both streets, potentially requiring the track relocation. These subdivision variances were submitted to the West Lafayette Board of Public Works and Safety and at its May 8th meeting the Board voted to recommend approval of both requests.

Along with the 36 lots in the Charles W. Ross Addition, the plat includes rights-of-way of two streets with connecting alleys – Hayes and Raymond Streets. Petitioner has started the process to vacate all of these public ways. On June 4th, the West Lafayette Common Council is scheduled to have the second reading on Ordinance No. 11-18, and if approved will vacate these rights-of-way.

Sidewalks along the north side of Meridian and south side of Leslie Avenue are currently located outside the street right-of-way. Staff recommends that sidewalk easements be shown on the final plat to cover these existing features.

**ENVIRONMENTAL AND UTILITY CONSIDERATIONS:**
The site is served by city sanitary sewer and the Indiana American Water Company.

**CONFORMANCE WITH UZO REQUIREMENTS:**
Most of the required building setbacks have been shown correctly. Because Meridian Street is classified as an urban secondary arterial, a 40-ft building setback is required as opposed to the 25-ft setback shown.

Petitioner has submitted an application for height, parking, vegetative and building coverage zoning variances to allow the construction of an aquatic center addition. These zoning variances are set to be heard at the May 23rd hearing of the Area Board of Zoning Appeals.

**STAFF RECOMMENDATION:**
Conditional primary approval, contingent on the following:

A. Subdivision Variances

1. A variance to not dedicate the additional 5-ft of right-of-way required along the west side of Grant Street.

2. A variance to not dedicate the additional 10-ft right-of-way required along the north side of Meridian Street.

B. Conditions

**FINAL PLAT** – The following items shall be part of the Secondary Application and Final Plat approval:

1. Submit a copy of the West Lafayette Common Council approval of Ordinance No. 11-18, which vacates all public ways in the Charles W. Ross Addition.

2. If there is a mortgage on this property, a recorded partial release or written acknowledgment from the mortgage company must be obtained in order to dedicate the necessary right-of-way.

3. Pedestrian access easements shall be platted along the rights-of-way of the north side of Meridian Street and the south side of Leslie Avenue for the existing sidewalks.

4. All existing easements, covenants or restrictions shall be shown and referenced with the corresponding recording information (Document Number and date recorded).

5. All required building setbacks shall be platted.

6. The street addresses and County Auditor's Key Number shall be shown.